Folha Personalizada: 594 x 297mm

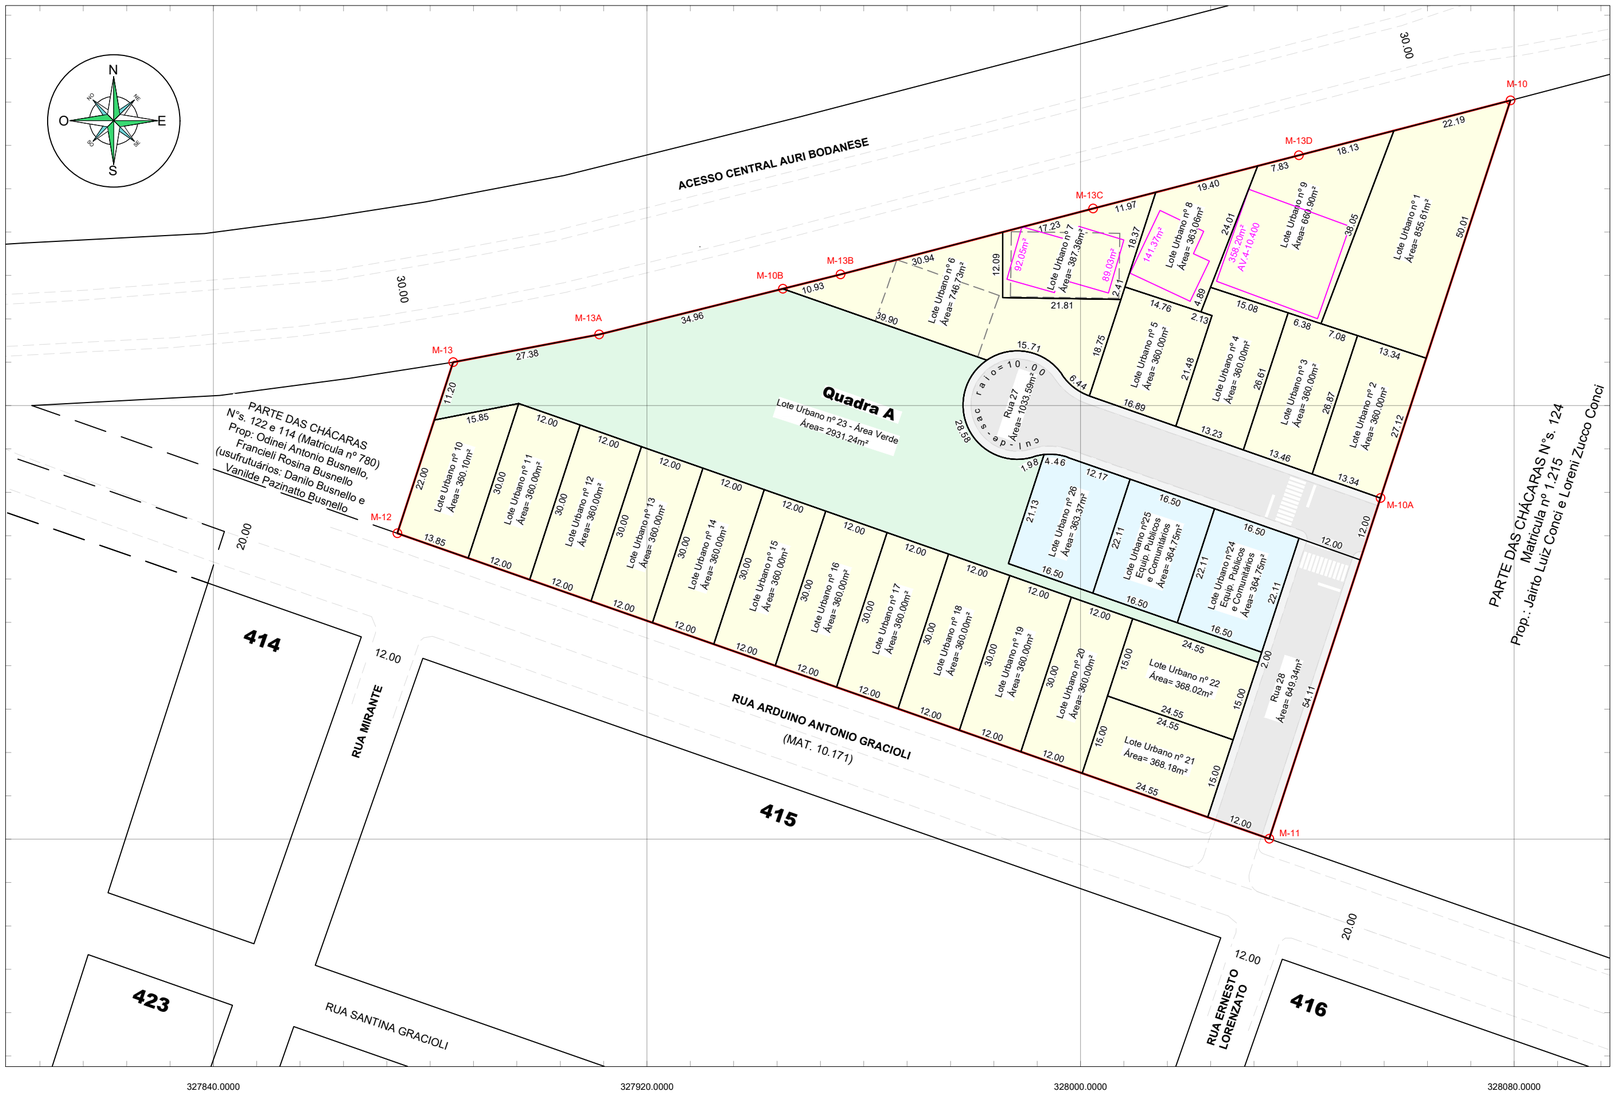

GEOMÉTRICO PROPOSTO - LOTEAMENTO TANGARÁ

ESCALA 1:800

DATUM HORIZONTAL: Sirgas 2000/ UTM zona 22s

COORDENADAS - MAT 10.400				
LADOS	AZIMUTES	DISTÂNCIA (m)	COORDENADAS (UTM)	
Vértice Vértice			E (m)	N (m)
M-10 M-10A	198°05'26"	77,13	328079,289	7041736,263
M-10A M-10B	289°17'52"	116,81	328055,337	7041662,941
M-10B M-13B	76°02'40"	10,89	327945,086	7041701,546
M-13B M-13C	75°23'51"	48,17	327955,693	7041704,182
M-13C M-13D	75°28'20"	39,21	328002,305	7041716,326
M-13D M-10	75°29'20"	40,32	328040,259	7041726,161

COORDENADAS - MAT 10.401				
LADOS	AZIMUTES	DISTÂNCIA (m)	COORDENADAS (UTM)	
Vértice Vértice			E (m)	N (m)
M-10A M-11	198°05'26"	66,12	328055,337	7041662,941
M-11 M-12	289°17'52"	170,43	328034,807	7041600,095
M-12 M-13	18°05'27"	33,20	327873,955	7041656,418
M-13 M-13A	79°10'48"	27,38	327884,264	7041687,975
M-13A M-10B	76°02'40"	35,00	327911,161	7041693,116
M-10B M-10A	109°17'52"	116,81	327945,086	7041701,546

QUADRO DE ÁREAS DAS MATRICULAS			
Descrição	Quantidades	Áreas (m²)	% sobre a gleba
Matrícula nº 10.400	1	4.500,00	30,29
Matrícula nº 10.401	1	10.357,00	69,71
Area Total	1	14.857,00	100,00

QUADRO DE ÁREAS DO LOTEAMENTO PROPOSTO			
Descrição	Quantidades	Áreas (m²)	% sobre a gleba
APP	-	-	-
Ruas	2	1.682,93	11,33
Equipamentos Publicos e Comunitários	3	1.092,87	7,35
Área Verde	1	2.931,24	18,73
Total de Áreas Públicas	6	5.707,04	38,41
Total de Lotes Habitacionais	22	9.149,96	61,59

LEGENDA:

- Ruas
- Equipamentos Publicos e Comunitários
- Áreas Verdes
- Lotes Habitacionais
- Curva de Nivel Mestre - 5,00m
- Curva de Nivel intermediária - 1,00m
- Perimetro Total do Loteamento
- Edificações existentes
- Meio-Fio

APROVAÇÃO:

PREFEITURA MUNICIPAL DE QUILOMBO, inscrita no CNPJ: 83.021.865/0001-61, com sede na R. Duque de Caxias, 165, Centro, Quilombo - SC, CEP: 89850-000, representada por seu responsável técnico, declara o presente projeto aprovado em fase de **CONSULTA PREVIA.**

Assinatura do Responsável Técnico do Município

ASSINATURA DOS PROPRIETÁRIOS:

Quilombo/SC, 01 de outubro de 2024.

DANILO BUSNELLO	VENILDE PAZINATTO BUSNELLO	SIDINEI P. FRANÇA & CIA LTDA
CPF: 423.656.609-59	CPF: 019.252.309-02	CNPJ: 05.890.699/0001-26

ASSINATURA DO RESPONSÁVEL TÉCNICO:

Sandro Serafini, Engenheiro Civil (CREA 175240-3), de CPF n°. 102.416.149-88, portador do RG n°. 5.679.819 SESP/SC, brasileiro, solteiro, residente e domiciliado na Rua Pomerode, 780, Condominio Cristo Rei, apartamento n°. 206B, Bairro Cristo Rei, Chapecó - SC, endereço eletronico: authamapeamento@gmail.com.

Quilombo/SC, 01 de outubro de 2024.

Autha Engenharia e Mapeamento

SANDRO SERAFINI:10241614988

Assinado de forma digital por SANDRO SERAFINI:10241614988
Dados: 2024.10.18 15:47:54 -03'00'

SANDRO SERAFINI
Engenheiro Civil
CREA/SC - 175240-3

GEOMÉTRICO - LOTEAMENTO TANGARÁ

Loteamento Convencional com Uso Predominantemente Residencial

Parte das Chácaras nº 123 e 115, Matrículas nº 10.400 e 10.401 ORI Quilombo-SC

Para acessar o projeto escaneie o qr code:

PROPRIETÁRIO(S): Danilo Busnello e Vanilde Pazinato Busnello, SIDINEI P. FRANÇA & CIA LTDA

ÁREA DO PROJETO: 14.857,00 m²

ENDEREÇO: Acesso Central Auri Bodanese, Bairro Industrial, Quilombo-SC

ESCALA: Indicada

CONTEÚDO: - Situação Atual das Matriculas - Levantamento Planialtimétrico

DESENHO: Sandro Serafini (Eng. Civil - CREA/SC:175240-3)

PASTA: OneDrive\Projetos\2022\LOTEAMENTO BUSNELLO

REVISÃO:	ALTERAÇÃO:	DATA:

FOLHA: **01/01**

Em respeito a Lei nº 13.709, de 14 de agosto de 2018, Lei Geral de Proteção de Dados (LGPD), este documento pode conter informações confidenciais. Qualquer uso não autorizado, cópia ou distribuição do seu conteúdo é estritamente proibido e pode ser ilegal.