FOLHA PERSONALIZADA: 592x594mm

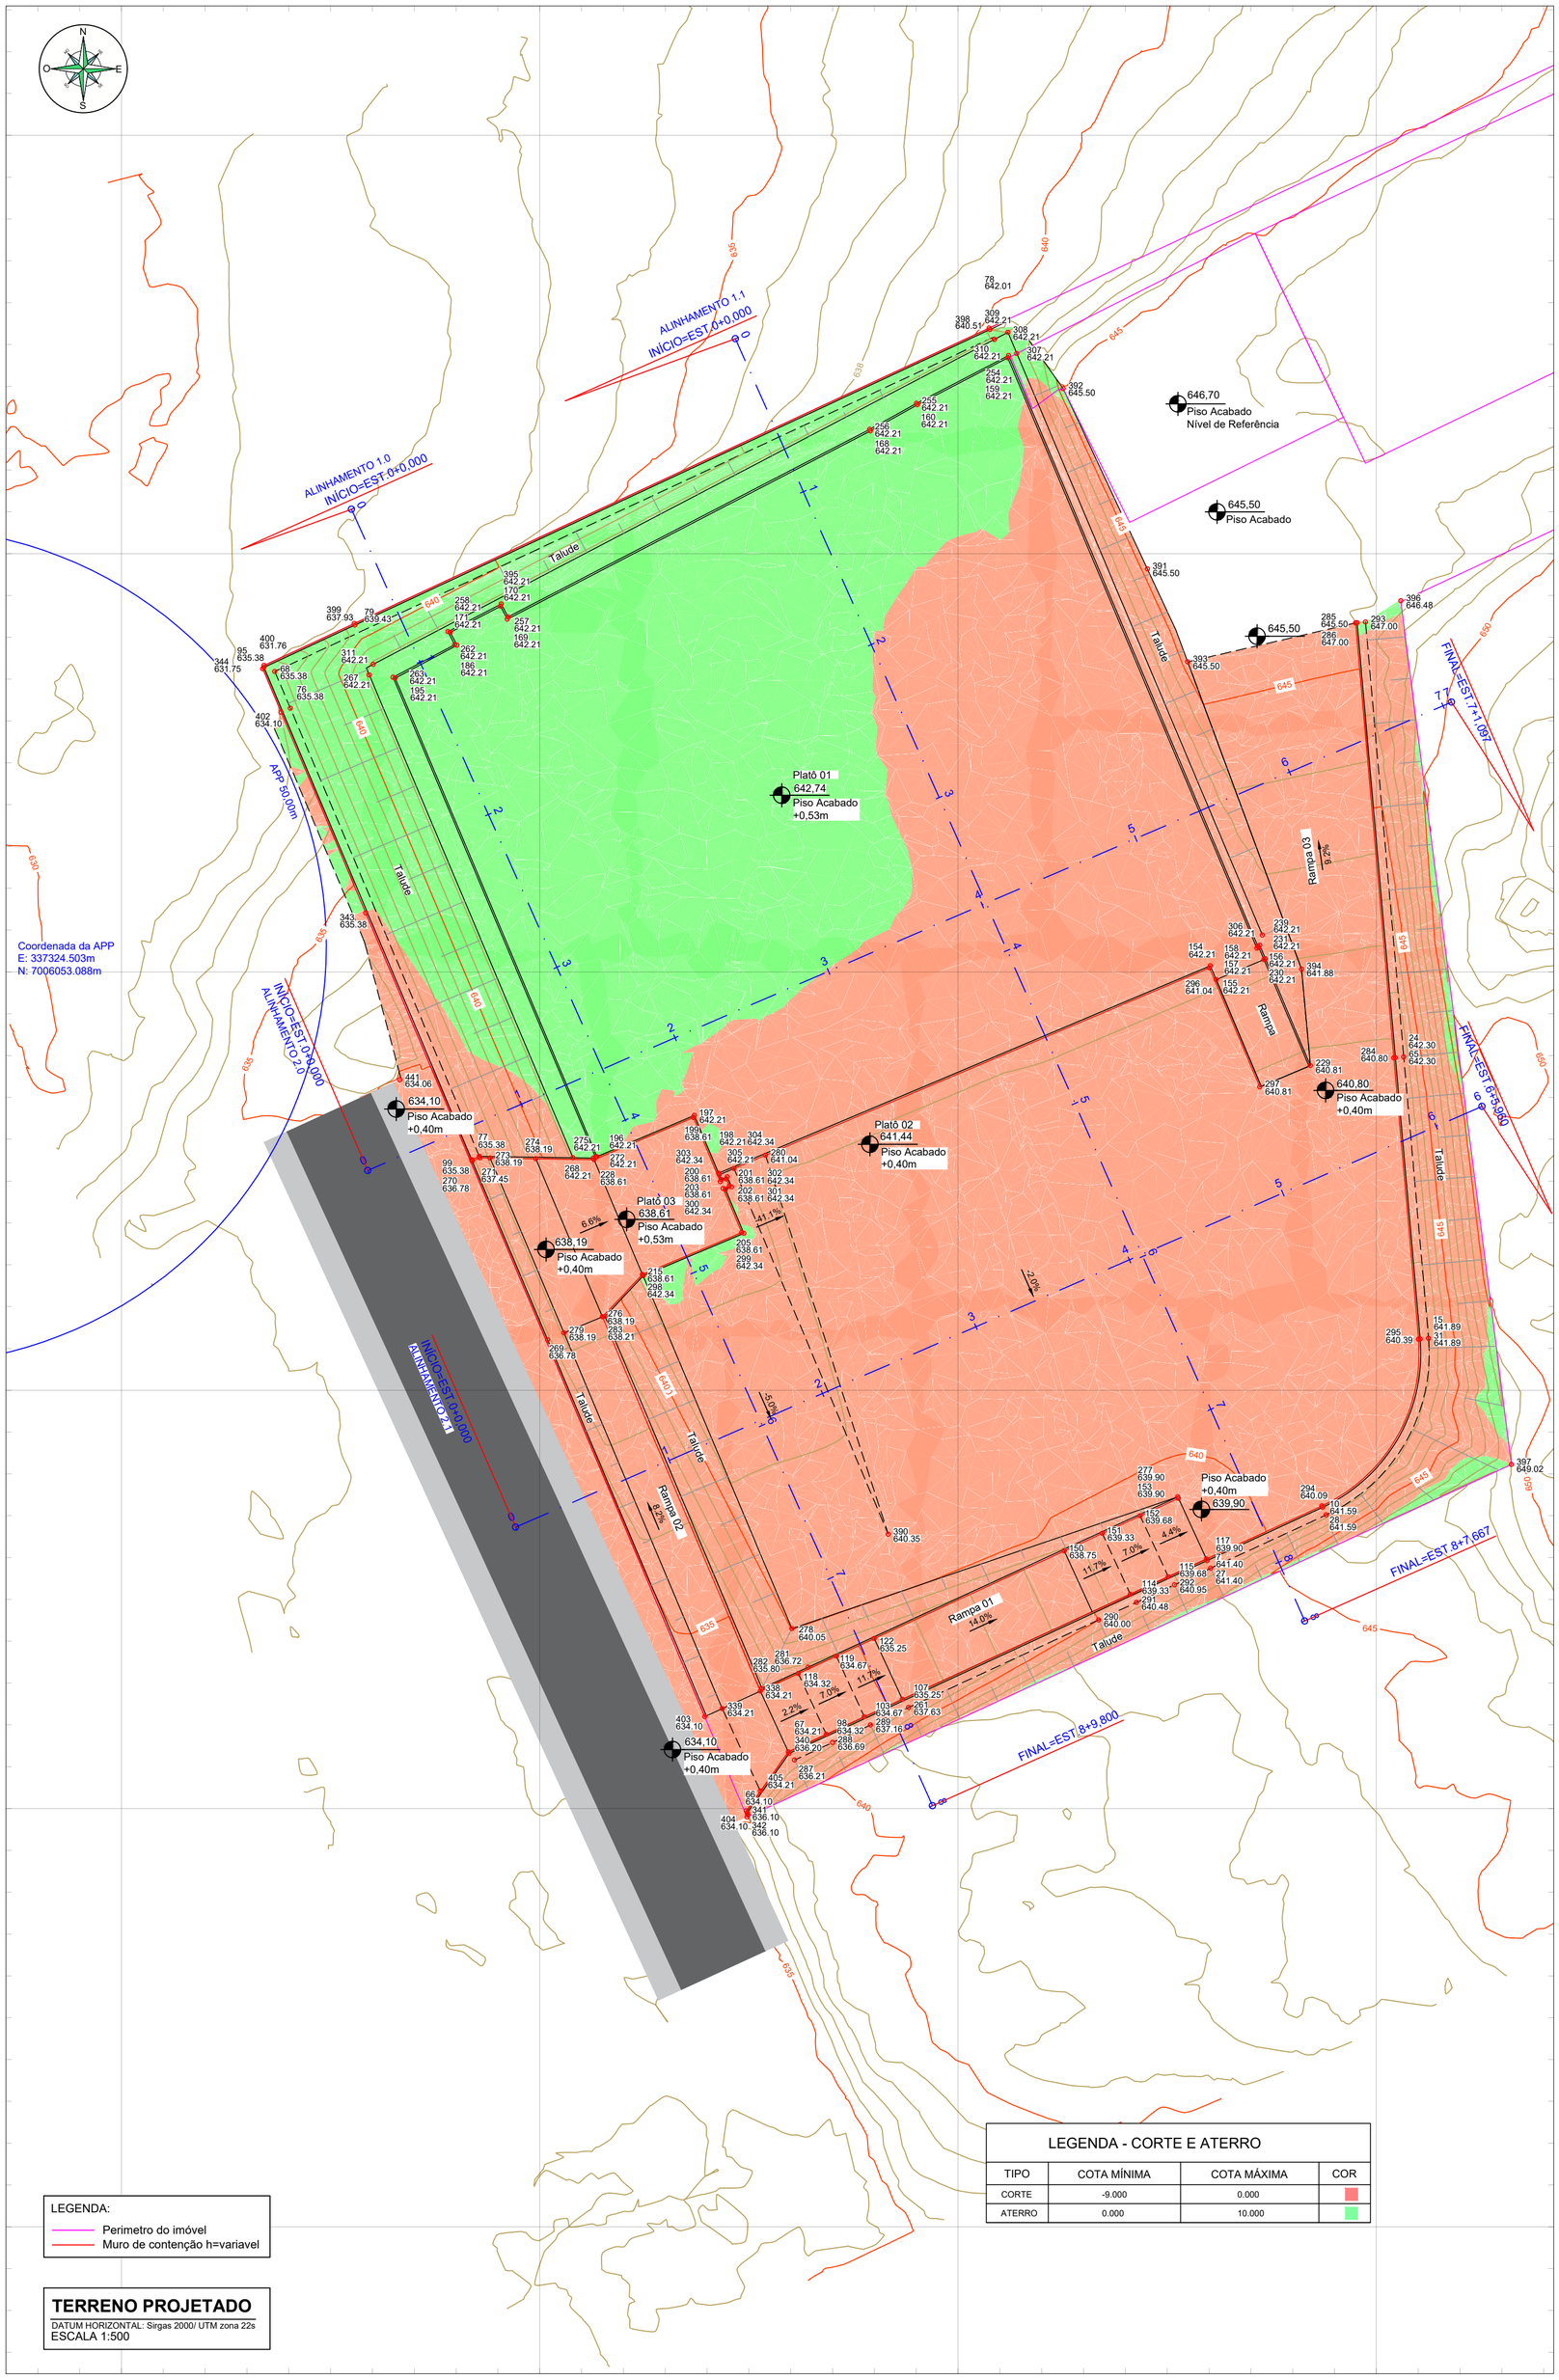

TABELA DE COORDENADAS			
PONTO No,	NORTE	ESTE	ELEVAÇÃO
7	7.005.979,64	337.479,78	641.40
10	7.005.986,00	337.493,57	641.59
15	7.006.006,11	337.505,24	641.89
24	7.006.039,75	337.502,28	642.30
27	7.005.978,73	337.480,20	641.40
28	7.005.985,09	337.493,99	641.59
31	7.006.006,20	337.506,23	641.89
65	7.006.039,84	337.503,27	642.30
66	7.005.949,73	337.424,69	634.10
67	7.005.956,78	337.429,72	634.21
68	7.006.085,90	337.368,35	635.38
76	7.006.081,51	337.370,21	635.38
77	7.006.027,95	337.392,79	635.38
78	7.006.126,76	337.453,81	642.01
79	7.006.091,45	337.377,92	639.43
95	7.006.086,40	337.367,06	635.38
98	7.005.958,87	337.434,26	634.32
99	7.006.027,56	337.391,87	635.38
103	7.005.960,97	337.438,81	634.67
107	7.005.963,06	337.443,35	635.25
114	7.005.975,62	337.470,59	639.33
115	7.005.977,72	337.475,13	639.68
117	7.005.979,82	337.479,70	639.90
118	7.005.966,14	337.430,91	634.32
119	7.005.968,23	337.435,46	634.67
122	7.005.970,32	337.440,00	635.25
150	7.005.980,79	337.462,70	638.75
151	7.005.982,89	337.467,24	639.33
152	7.005.984,98	337.471,78	639.68
153	7.005.987,09	337.476,35	639.90
154	7.006.050,73	337.480,16	642.21
155	7.006.049,07	337.480,86	642.21
156	7.006.051,48	337.486,56	642.21
157	7.006.052,92	337.485,96	642.21
158	7.006.052,82	337.485,71	642.21
159	7.006.123,38	337.455,95	642.21
160	7.006.117,78	337.445,14	642.21
168	7.006.114,66	337.439,53	642.21
169	7.006.092,15	337.396,14	642.21
170	7.006.093,69	337.395,33	642.21
171	7.006.090,58	337.389,32	642.21
186	7.006.089,03	337.390,12	642.21
195	7.006.085,11	337.382,74	642.21
196	7.006.027,92	337.406,85	642.21
197	7.006.032,85	337.418,49	642.21
198	7.006.025,94	337.421,39	642.21
199	7.006.032,59	337.418,38	638.61
200	7.006.024,93	337.421,60	638.61
201	7.006.025,24	337.422,32	638.61
202	7.006.024,41	337.422,67	638.61
203	7.006.024,10	337.421,94	638.61
205	7.006.018,85	337.424,15	638.61
215	7.006.013,85	337.412,29	638.61
228	7.006.027,56	337.406,50	638.61
229	7.006.038,80	337.492,12	640.81
230	7.006.051,55	337.486,75	642.21

TABELA DE COORDENADAS			
PONTO No,	NORTE	ESTE	ELEVAÇÃO
231	7.006.053,18	337.486,06	642.21
239	7.006.053,08	337.485,82	642.21
254	7.006.123,66	337.456,05	642.21
255	7.006.117,95	337.445,05	642.21
256	7.006.114,83	337.439,44	642.21
257	7.006.092,42	337.396,22	642.21
258	7.006.090,67	337.389,05	642.21
261	7.005.962,08	337.444,09	637.63
262	7.006.089,11	337.389,85	642.21
263	7.006.085,20	337.382,48	642.21
267	7.006.085,49	337.379,65	642.21
268	7.006.027,78	337.403,98	642.21
269	7.006.006,03	337.400,95	636.78
270	7.006.027,38	337.391,95	636.78
271	7.006.027,76	337.392,87	637.45
272	7.006.027,84	337.406,67	642.21
273	7.006.027,75	337.394,08	638.19
274	7.006.027,66	337.399,54	638.19
275	7.006.027,74	337.406,43	642.21
276	7.006.008,79	337.407,50	638.19
277	7.005.987,27	337.476,26	639.90
278	7.005.971,50	337.430,14	640.05
279	7.006.006,85	337.402,90	638.19
280	7.006.028,09	337.426,99	641.04
281	7.005.966,90	337.432,09	636.72
282	7.005.964,35	337.426,57	635.80
283	7.006.008,83	337.407,81	638.21
284	7.006.039,73	337.502,08	640.80
285	7.006.091,71	337.497,51	645.50
286	7.006.091,72	337.497,71	647.00
287	7.005.955,80	337.430,47	636.21
288	7.005.957,90	337.435,01	636.69
289	7.005.959,99	337.439,55	637.16
290	7.005.972,55	337.466,80	640.00
291	7.005.974,64	337.471,34	640.48
292	7.005.976,74	337.475,88	640.95
293	7.006.091,81	337.498,70	647.00
294	7.005.986,18	337.493,49	640.09
295	7.006.006,10	337.505,04	640.39
296	7.006.050,47	337.480,05	641.04
297	7.006.036,24	337.486,05	640.81
298	7.006.013,66	337.412,36	642.34
299	7.006.018,74	337.424,41	642.34
300	7.006.023,99	337.422,21	642.34
301	7.006.024,30	337.422,93	642.34
302	7.006.025,50	337.422,43	642.34
303	7.006.025,19	337.421,70	642.34
304	7.006.025,76	337.421,46	642.34
305	7.006.026,50	337.423,23	642.21
306	7.006.054,39	337.486,37	642.21
307	7.006.123,91	337.457,03	642.21
308	7.006.126,43	337.455,97	642.21
309	7.006.125,59	337.454,36	642.21
310	7.006.125,59	337.454,35	642.21
311	7.006.086,76	337.380,11	642.21
338	7.005.964,04	337.426,37	634.21

TABELA DE COORDENADAS			
PONTO No,	NORTE	ESTE	ELEVAÇÃO
339	7.005.961,95	337.421,83	634.21
340	7.005.956,60	337.429,81	636.20
341	7.005.949,47	337.424,80	636.10
342	7.005.949,26	337.424,89	636.10
343	7.006.057,04	337.379,22	635.38
344	7.006.086,23	337.366,91	631.75
390	7.005.982,78	337.441,67	640.35
391	7.006.098,17	337.472,63	645.50
392	7.006.119,70	337.462,57	645.50
393	7.006.087,05	337.477,46	645.50
394	7.006.050,32	337.491,06	641.88
395	7.006.093,96	337.395,42	642.21
396	7.006.094,35	337.502,93	646.48
397	7.005.991,12	337.516,14	649.02
398	7.006.126,94	337.453,72	640.51
399	7.006.091,63	337.377,84	637.93
400	7.006.086,62	337.367,06	631.76
402	7.006.081,04	337.369,10	634.10
403	7.005.960,98	337.419,73	634.10
404	7.005.949,00	337.424,79	634.10
405	7.005.952,09	337.426,38	634.21
441	7.006.037,10	337.383,29	634.06

ESPAÇO RESERVADO A APROVAÇÃO DO MUNICÍPIO:

ASSINATURA DO REQUERENTE:

Chapecó/SC, 27 de janeiro de 2026.

Id Participacoes LTDA
CNPJ: 02.747.247/0001-00

ASSINATURA DO RESPONSÁVEL TÉCNICO:

Chapecó/SC, 27 de janeiro de 2026.

Autha
Engenharia e Mapeamento

SANDRO SERAFINI:10241614988

Assinado de forma digital por SANDRO SERAFINI:10241614988
Dados: 2026.02.04 12:42:22 -03'00'

SANDRO SERAFINI
Engenheiro Civil CREA/SC 175.240-3

LEGENDA - CORTE E ATERRO			
TIPO	COTA MÍNIMA	COTA MÁXIMA	COR
CORTE	-9.000	0.000	
ATERRO	0.000	10.000	

LEGENDA:
- Perimetro do imóvel
- Muro de contenção h=variavel

TERRENO PROJETADO
DATUM HORIZONTAL: Sirgas 2000/ UTM zona 22s
ESCALA 1:500

PROJETO GEOMÉTRICO DE TERRAPLENAGEM

ÁREA DE TERRA (MATRICULA 64.812 ORI Chapecó-SC)

PROPRIETÁRIO(S): Id Participacoes LTDA
ÁREA DO PROJETO: 17.050,00m²
ENDEREÇO: Rod. Plínio Arlindo de Nês, 911E - Belvedere, Chapecó - SC, 89805-290
ESCALA: Indicada
CONTEÚDO: - TERRENO PROJETADO
DESENHO: Sandro Serafini (Engenheiro Civil - CREA/SC : 175240-3)
PASTA: OneDrive\Projetos\2024\Terraplenagem_Loris Bigolin

REVISÃO:	ALTERAÇÃO:	DATA:
rev 01	Inserção de APP e adequação de aterros	27/01/2026

FOLHA: 03/04

Em respeito à Lei nº 13.709, de 14 de agosto de 2018, Lei Geral de Proteção de Dados (LGPD), este documento pode conter informações confidenciais. Qualquer uso não autorizado, cópia ou distribuição do seu conteúdo é estritamente proibido e pode ser ilegal.