Folha A1: 841 x 594 mm

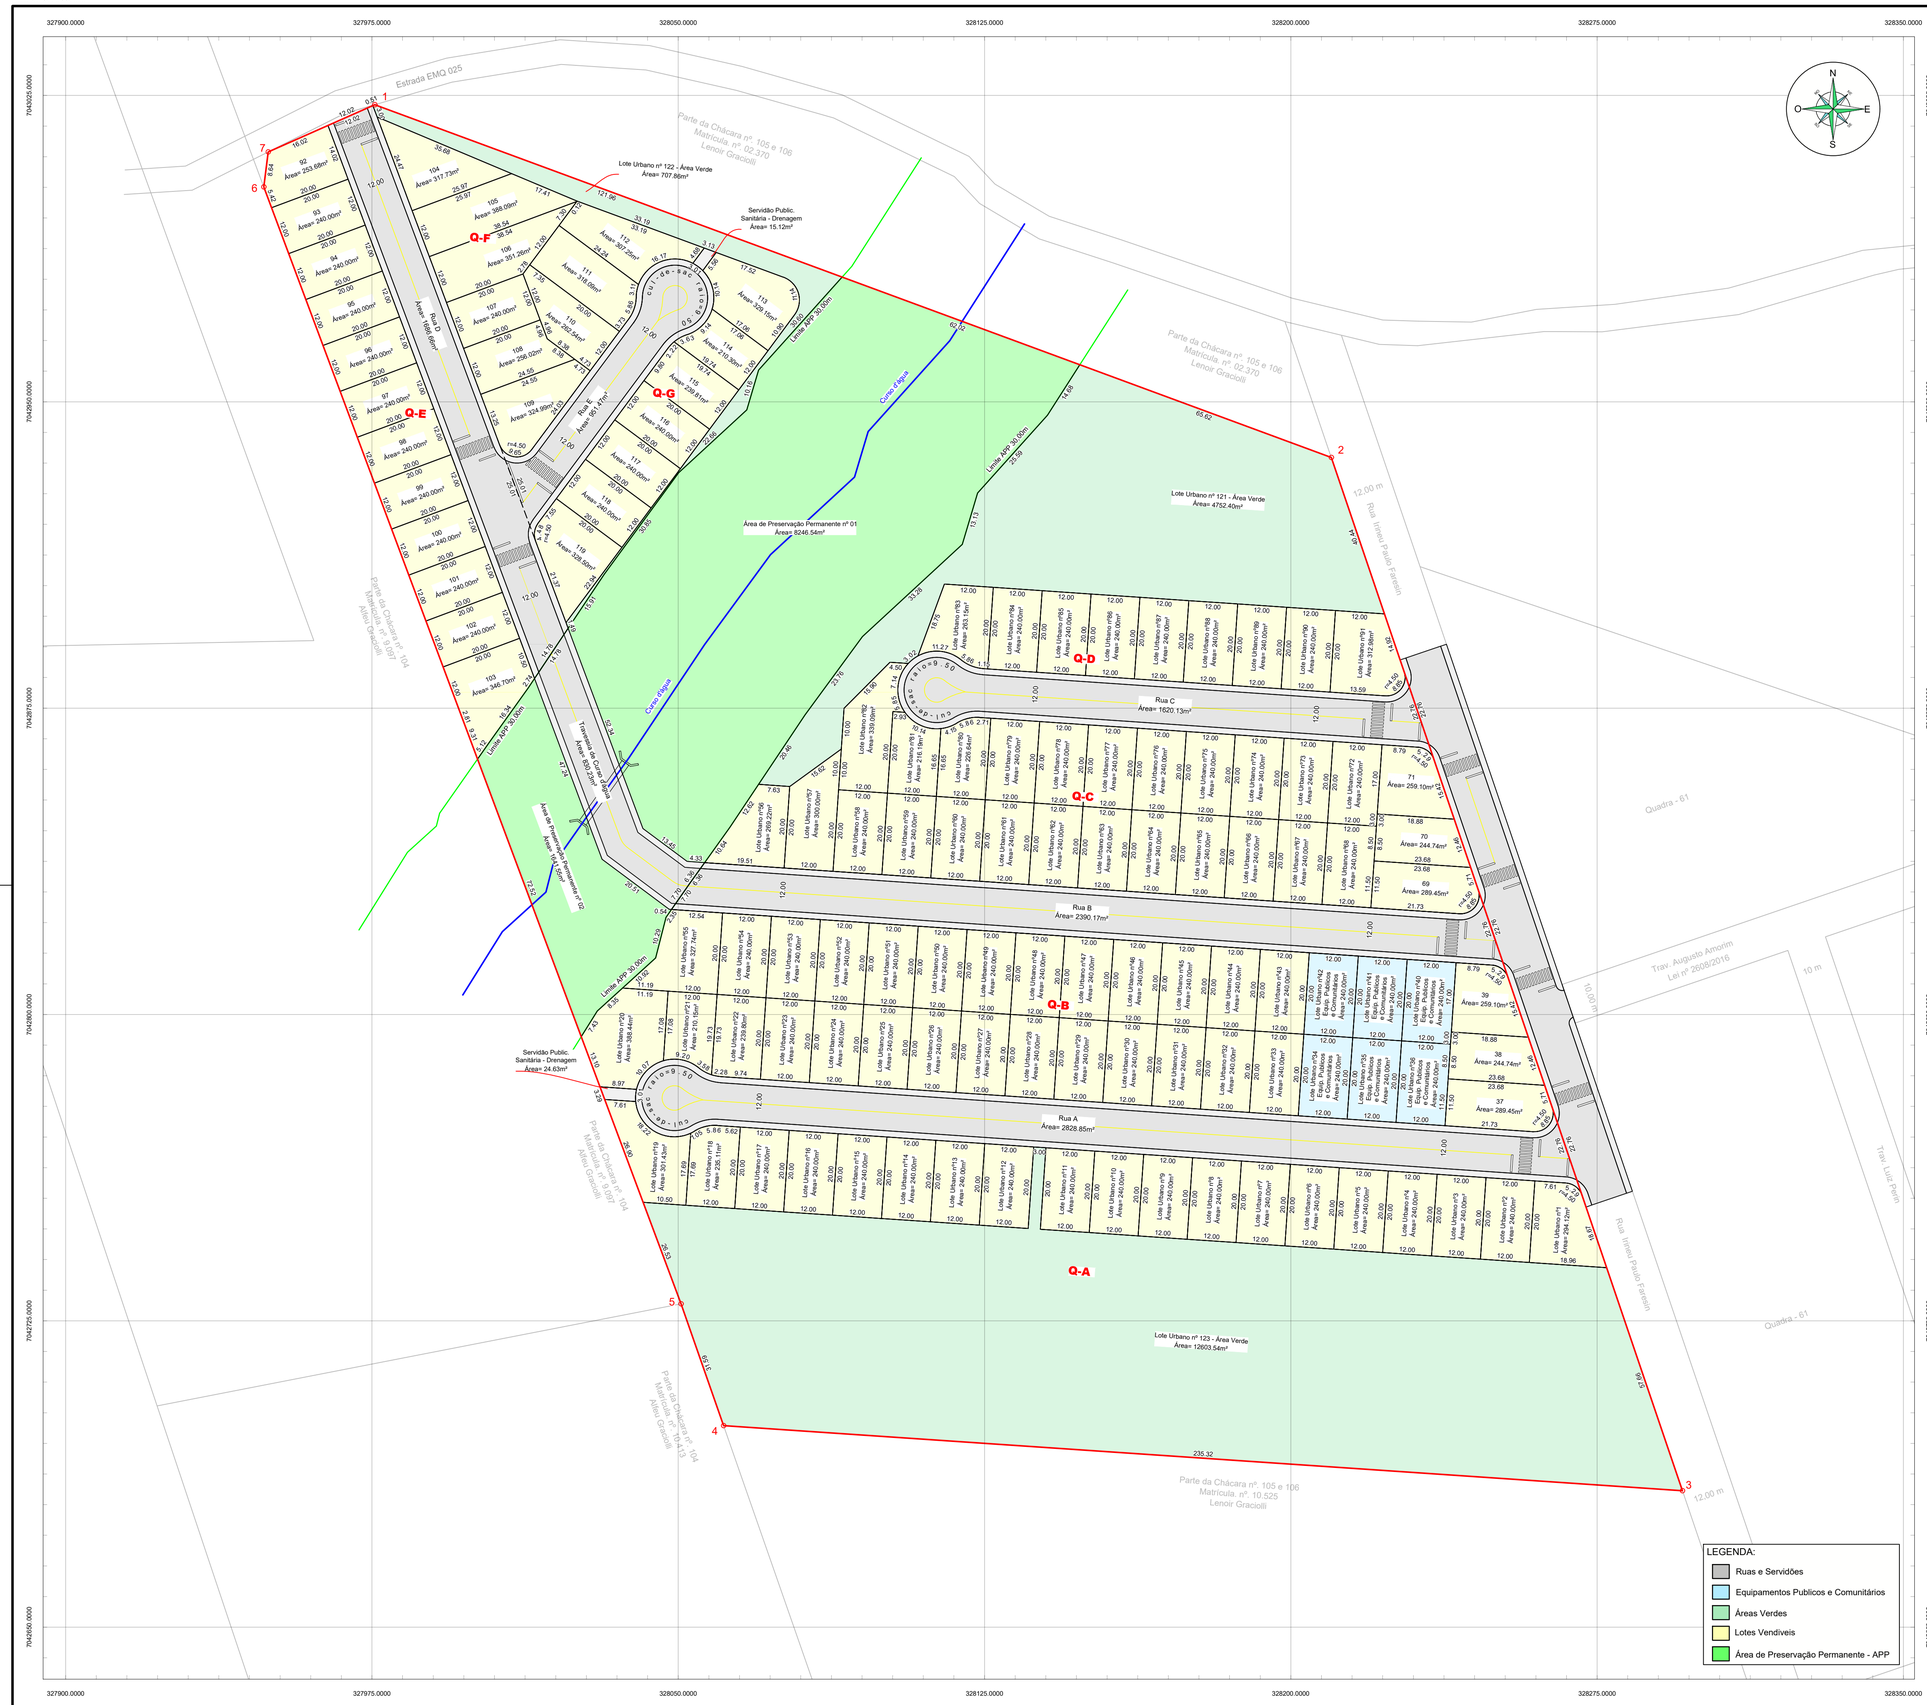

URBANISTICO PROPOSTO - LOTEAMENTO POPULAR AMORIM

ESCALA 1:750

DATUM HORIZONTAL: Sirgas 2000/ UTM zona 22s

QUADRO DE COORDENADAS				
LADOS		AZIMUTES	DISTANCIA (m)	COORDENADAS (UTM)	
Vértices	Vértices			N (metros)	E (metros)
1	2	110°14'23"	249,60	7.043.022,707	327.975,710
2	3	161°13'34"	267,15	7.042.936,358	328.209,899
3	4	273°52'48"	235,32	7.042.683,424	328.295,876
4	5	340°45'25"	31,59	7.042.699,347	328.061,096
5	6	339°30'46"	291,87	7.042.729,171	328.050,685
6	7	7°09'14"	8,64	7.043.002,581	327.948,530
7	1	66°07'37"	28,55	7.043.011,154	327.949,606

QUADRO DE ÁREAS DA MATRICULA			
Descrição	Quantidades	Áreas (m²)	% sobre a gleba
Gleba Loteamento	1	68.844,06	100,00
APP	1	10.718,32	15,66
Área Util	1	57.725,74	84,34
CÁLCULO DA ÁREA DE DOAÇÃO			
Descrição	Quantidades	Áreas (m²)	% sobre a area util
Área Util	1	57.725,74	100,00
Total de Área Publica a ser Doada	1	20.204,01	35,00

QUADRO DE ÁREAS DO LOTEAMENTO PROPOSTO			
Descrição	Quantidades	Áreas (m²)	% sobre a gleba
Gleba Loteamento	1	68.844,06	100,00
APP (com supressão da rua)	2	9.888,09	14,45
Área Util do Loteamento	1	58.555,97	85,55

QUADRO DE ÁREAS DO LOTEAMENTO PROPOSTO				
Descrição	Quantidades	Áreas (m²)	% sobre a área util	% sobre a gleba
APP (com supressão da rua)	2	9.888,09	-	14,45
Ruas e Servidões	7	10.347,27	17,67	15,12
Equipamentos Publicos e Comunitários	6	1.440,00	2,46	2,10
Área Verde	3	18.063,98	30,85	26,39
Total de Áreas Públicas	11	29.851,25	50,98	43,61
Total de Lotes Habitacionais	115	28.704,72	49,02	41,94

NOTAS, CARIMBOS, SELOS E APROVAÇÕES:

APROVAÇÃO:

PREFEITURA MUNICIPAL DE QUILOMBO, inscrita no CNPJ: 83.021.865/0001-61, com sede na R. Duque de Caxias, 165, Centro, Quilombo - SC, CEP: 89850-000, representada por seu responsável técnico, declara o presente projeto aprovado em fase de **CONSULTA PREVIA.**

Assinatura do Responsável Técnico do Município

ASSINATURA DO PROPRIETÁRIO:

JOSÉ CARLOS AMORIM, inscrito(a) no CPF sob nº. 219.214.409-10, portador(a) da CI RG nº. 457.099 SSP/SC, empresário, nascido em 08/03/1955, residente e domiciliado na Avenida Coronel Ernesto Francisco Bertaso, nº. 444, Centro, nesta Cidade de Quilombo - SC.

Quilombo/SC, 01 de outubro de 2024.

JOSÉ CARLOS AMORIM
CPF: 219.214.409-10

ASSINATURA DO RESPONSÁVEL TÉCNICO:

Sandro Serafini, Engenheiro Civil (CREA: 175240-3), de CPF nº. 102.416.149-88, portador do RG nº. 5.679.819 SESP/SC, brasileiro, solteiro, residente e domiciliado na Rua Pomerode, 780, Condomínio Cristo Rei, apartamento nº. 206B, Bairro Cristo Rei, Chapecó - SC, endereço eletronico: authamapeamento@gmail.com.

Quilombo/SC, 01 de outubro de 2024.

Autha
Engenharia e Mapeamento

SANDRO SERAFINI
Engenheiro Civil
CREA/SC - 175240-3

GEOMÉTRICO - LOTEAMENTO POPULAR AMORIM
Loteamento de Modalidade Popular com Uso Predominantemente Residencial
Parte das Chácaras nº 105 e 106, Matrícula nº 10.690 CRI Quilombo-SC

Para acessar o projeto escaneie o qr code:

PROPRIETÁRIO(S): José Carlos Amorim

ÁREA DO PROJETO: 68.444,06 m²

ENDEREÇO: Travessa Irineu Paulo Foresin, Bairro Industrial, Quilombo-SC

ESCALA: Indicada

CONTEÚDO: - Urbanistico Proposto - Loteamento Popular Amorim

DESENHO: Sandro Serafini (Eng. Civil - CREA/SC:175240-3)

PASTA: OneDrive\Projetos\2023\LOTEAMENTO AMORIM

REVISÃO:	ALTERAÇÃO:	DATA:

FOLHA: **01/01**

Em respeito à Lei nº 13.709, de 14 de agosto de 2018, Lei Geral de Protecção de Dados (LGPD), este documento pode conter informações confidenciais. Qualquer uso não autorizado, cópia ou distribuição do seu conteúdo é estritamente proibido e pode ser legal.